


SHOP DRAWING THÉP SÀN (BY GIAHUY.NET)


1/1

Sàn S1 (SL=1; dày=100mm)

Bê tông B25 · Thép CB400-V · Lớp BV 25mm · Khổ A1

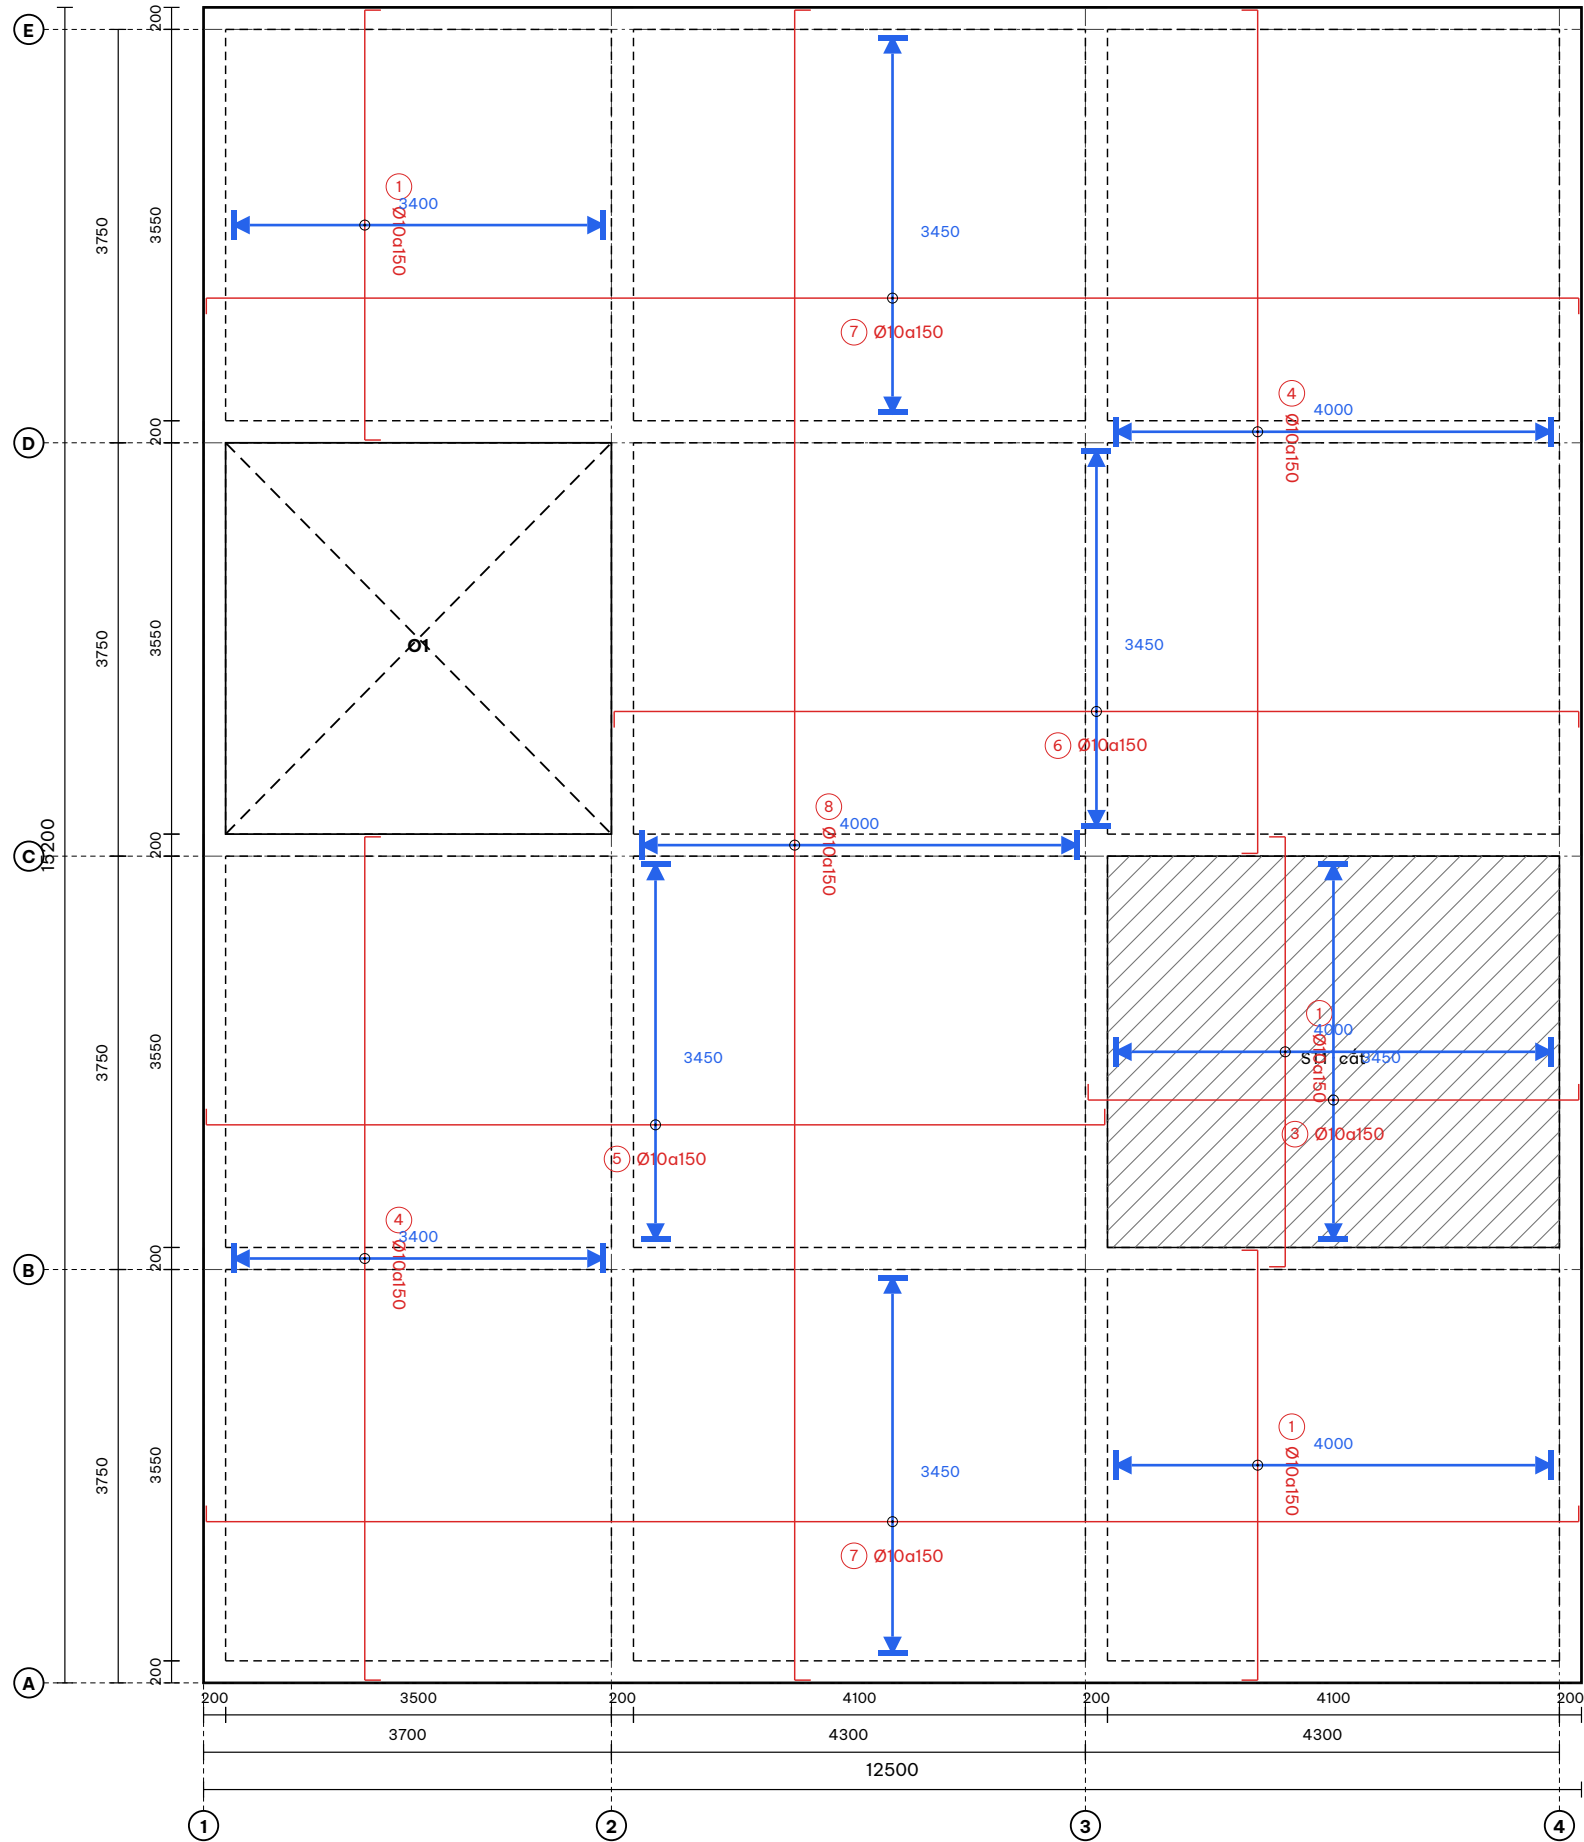


MẶT BẰNG CỐT THÉP SÀN LỚP DƯỚI
TL: 1/100

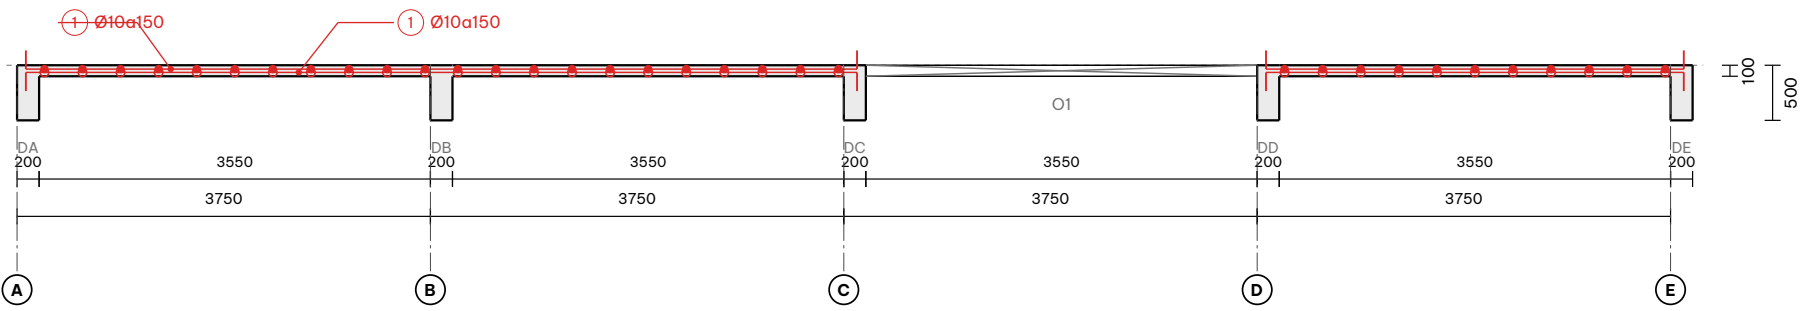


MẶT CẮT THÉP SÀN A-A

TL: 1/100 · Lớp BV 25
Cắt theo phương X-X=1850 (trục 1) · trục A-E

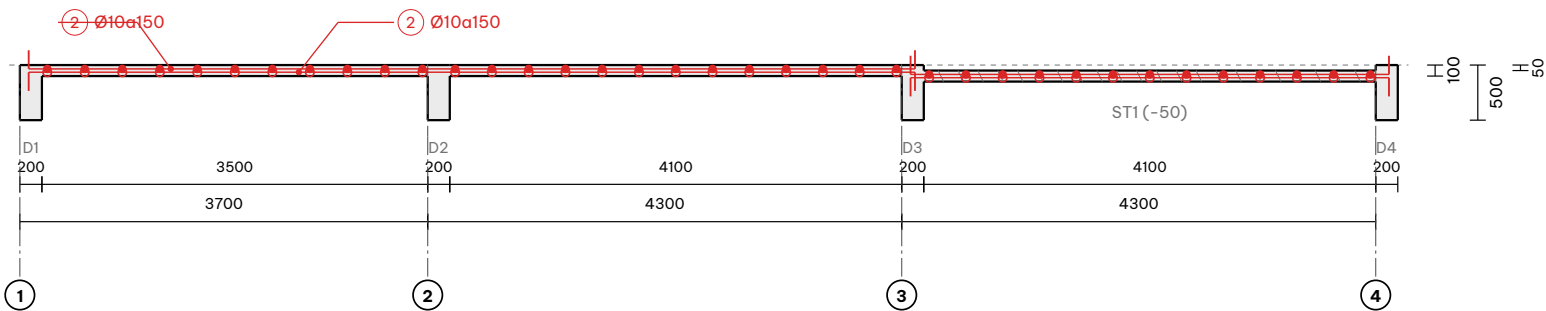

MẶT CẮT THÉP SÀN B-B

TL: 1/100 · Lớp BV 25
Cắt theo phương Y-Y=5600 (trục B) · trục 1-4

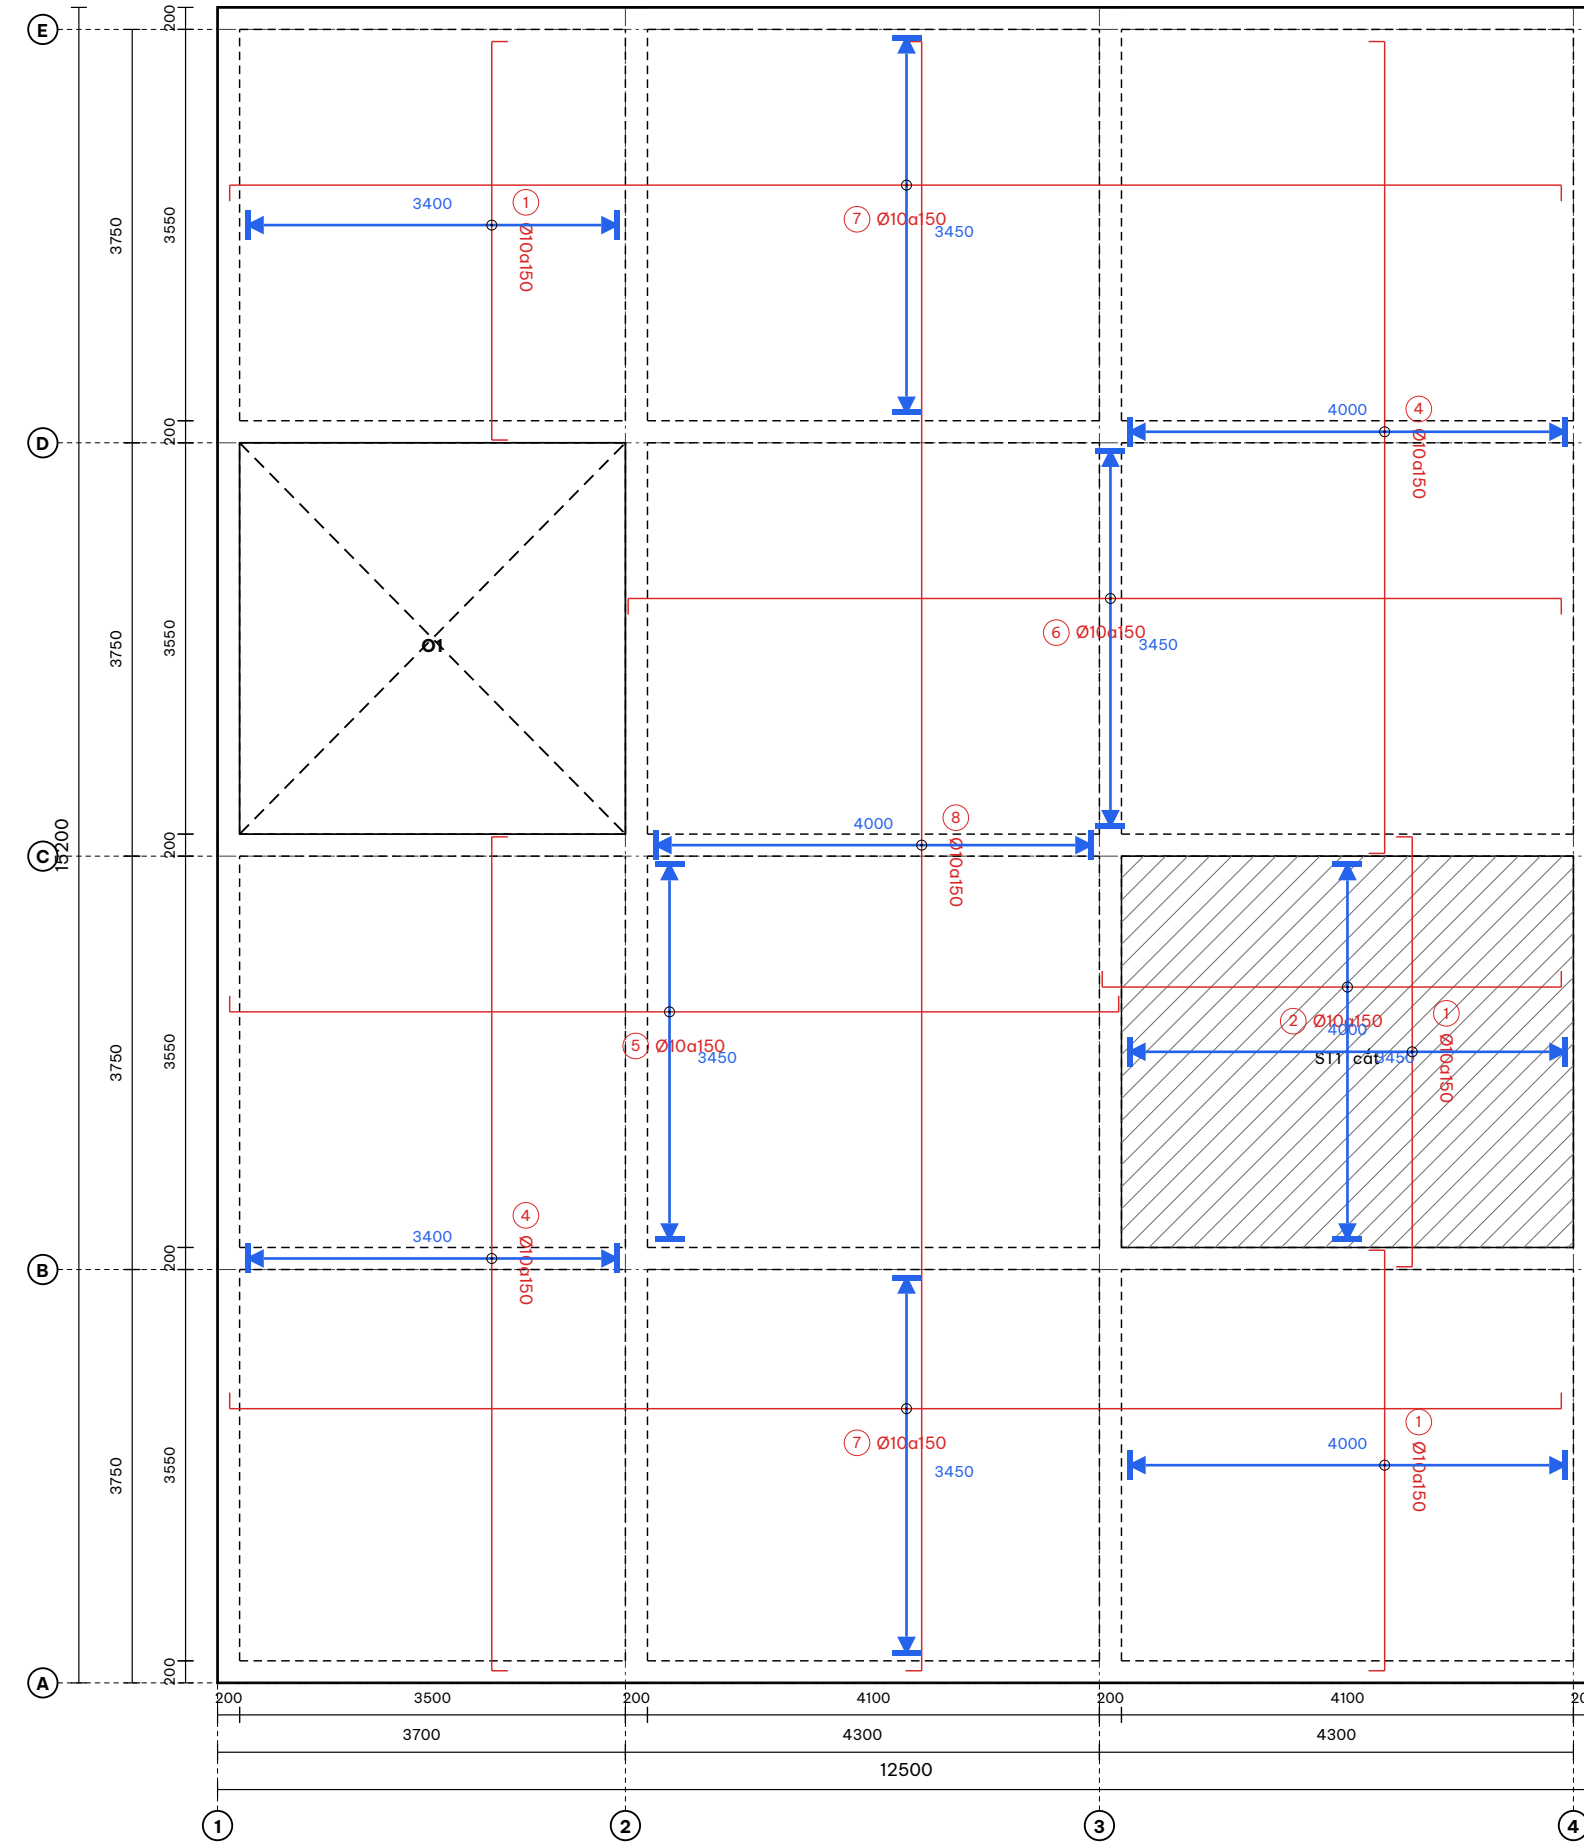

MẶT BẰNG CỐT THÉP SÀN LỚP TRÊN
TL: 1/100

BẢNG THỐNG KÊ CỐT THÉP SÀN

TÊN CK	STT	HÌNH DẠNG	Ø	DÀI l	SL CK	1 CK	TỔNG	DÀI (m)	KG
Sàn S1	1		10	4100	1	102	102	418.2	257.83
	2		10	4365	1	23	23	100.39	61.9
	3		10	4650	1	23	23	106.95	65.94
	4		10	7850	1	102	102	800.7	493.65
	5		10	8350	1	50	50	417.5	257.4
	6		10	8950	1	50	50	447.5	275.89
	7		10	12650	1	96	96	1214.4	748.71
	8		10	15350	1	58	58	890.3	548.89

TỔNG HỢP CỐT THÉP

ĐƯỜNG KÍNH (mm):	Ø10
CHIỀU DÀI (m):	4395.94
TRỌNG LƯỢNG (kg):	2710.2
SỐ THANH 11.7m:	—

Tổng TL: 2710.2 kg